


MULTI-ZONE AIR CONDITIONING — SAMPLE FLOOR PLAN

4 office zones + corridor return • 1× AHU (15,000 CFM) + 9× FCUs • Chilled-water primary plant (2× 150 TR + induced-draft tower)

DEMO / PITCH REFERENCE — NOT FOR CONSTRUCTION

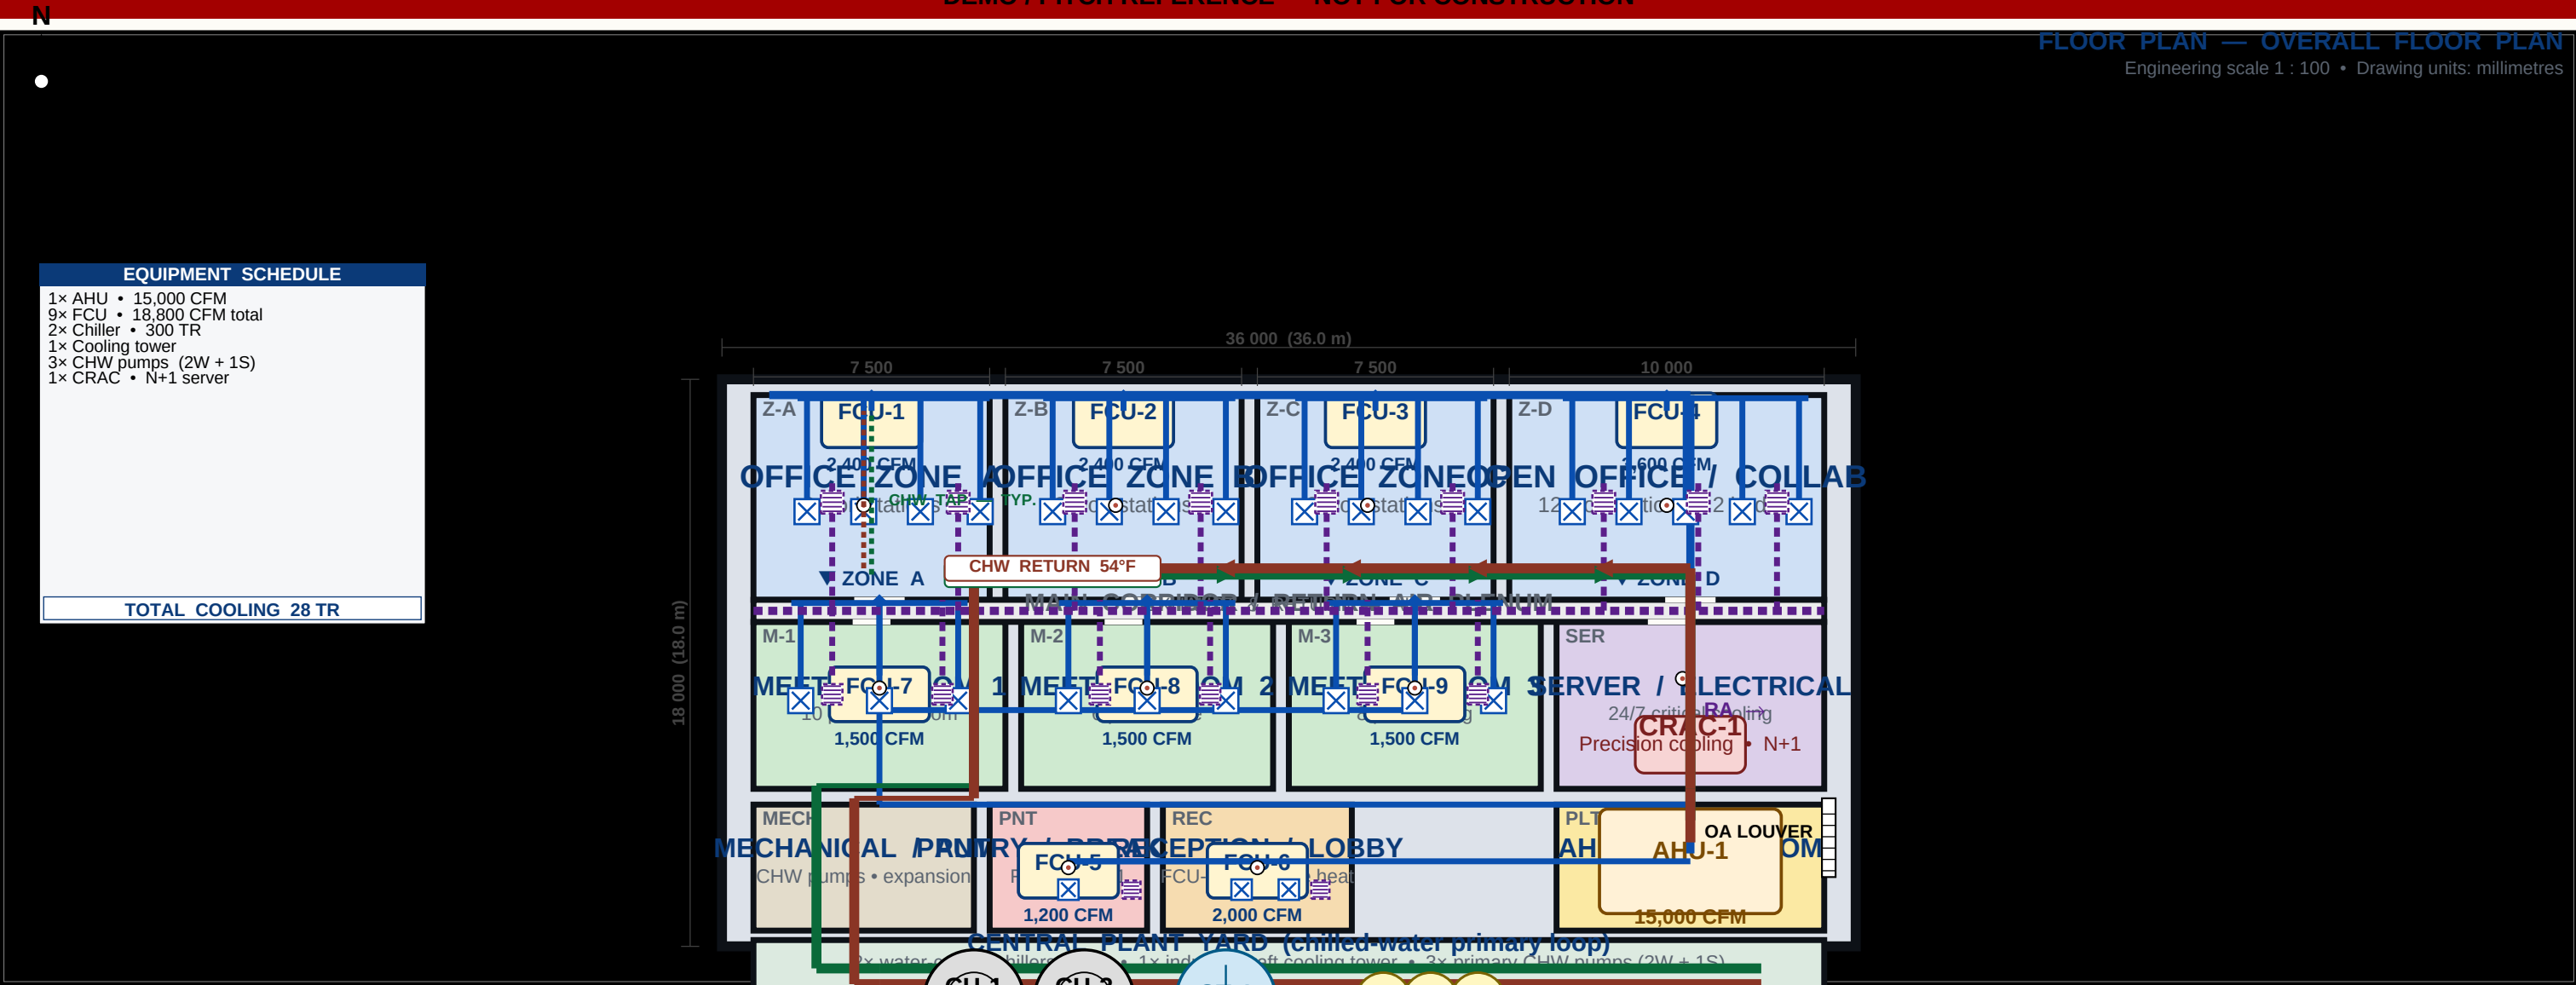

Alnchors

OVERALL FLOOR PLAN

DATE
2026-07-20
REV. B (A3 multipage)

LEGEND

- Office zone
- Meeting / training
- Server / electrical
- AHU plant room
- Mechanical / pump
- Pantry / breakout
- Reception / lobby
- Corridor / return plenum
- Central plant yard

- AHU Air-Handling Unit (AHU)
- FCU Fan-Coil Unit (FCU)
- Water-cooled chiller
- Cooling tower (induced draft)
- Precision cooling (server room)
- Primary chilled-water pump
- Supply diffuser (4-way)
- Return-air grille
- Zone thermostat (BACnet)

- Supply duct (cool air)
- Return duct (warm air)
- CHW supply 44°F / 7°C
- CHW return 54°F / 12°C
- Condenser water (CW)
- Building / partition wall
- Flow direction arrow
- North arrow

- Total cooling load (est.): 28 TR
- 1× AHU 15,000 CFM (4-zone VAV)
- 9× FCUs zone + meeting + amenity
- 2× 150 TR chillers (N+1)
- 1× induced-draft cooling tower
- 3× primary CHW pumps (2W + 1S)
- CHW ΔT 10°F (44°F / 54°F)
- OA: 20 CFM/person ASHRAE 62.1
- Filtration: MERV-13 (AHU) + MERV-8 (FCU)
- Controls: BACnet/Modbus DDC, VAV zone dampers
- Acoustics: NC-35 offices, NC-40 open zones
- Server room: dedicated CRAC N+1, 24/7


DEMO / PITCH REFERENCE — NOT FOR CONSTRUCTION

- AHU Air-Handling Unit
- FCU Fan-Coil Unit
- VAV Variable Air Volume
- CRAC Computer Room A/C
- CHW Chilled Water
- CW Condenser Water
- OA Outside Air
- RA Return Air
- SA Supply Air
- TR Ton of Refrigeration
- CFM Cubic Feet / Minute
- DDC Direct Digital Control
- MERV Minimum Efficiency Reporting Value
- NC Noise Criterion
- N+1 One redundant unit

MULTI-ZONE AIR CO

4 office zones + corridor return • 1× AHU (15,000

N

 

LEGEND

- Office zone
- Meeting / training
- Server / electrical
- AHU plant room
- Mechanical / pump
- Pantry / breakout
- Reception / lobby
- Corridor / return plenum
- Central plant yard

- AHU
- Fan-Coil Unit (FCU)
- Water-cooled chiller
- Cooling tower (induced draft)
- Precision cooling (server room)
- Primary chilled-water pump
- Supply diffuser (4-way)
- Return-air grille
- Zone thermostat (BACnet)

- Return duct (warm air)
- CHW supply 44°F / 7°C
- CHW return 54°F / 12°C
- Condenser water (CW)
- Building / partition wall
- Flow direction arrow
- North arrow


- 1× AHU 15,000 CFM (1 Zone VAV)
- 9× FCUs zone + meeting + amenity
- 2× 150 TR chillers (N+1)
- 1× induced-draft cooling tower
- 3× primary CHW pumps (2W + 1S)
- CHW ΔT 10°F (44°F / 54°F)
- OA: 20 CFM/person ASHRAE 62.1
- Filtration: MERV-13 (AHU) + MERV-8 (FCU)
- Controls: BACnet/Modbus DDC, VAV zone dampers
- Acoustics: NC-35 offices, NC-40 open zones
- Server room: dedicated CRAC N+1, 24/7

- FCU Fan-Coil Unit
- VAV Variable Air Volume
- CRAC Computer Room A/C
- CHW Chilled Water
- CW Condenser Water
- OA Outside Air
- RA Return Air
- SA Supply Air
- TR Ton of Refrigeration
- CFM Cubic Feet / Minute
- DDC Direct Digital Control
- MERV Minimum Efficiency Reporting Value
- NC Noise Criterion
- N+1 One redundant unit

MULTI-ZONE AIR COND

4 office zones + corridor return • 1× AHU (15,000 CFM)

N

 

LEGEND

- Office zone
- Meeting / training
- Server / electrical
- AHU plant room
- Mechanical / pump
- Pantry / breakout
- Reception / lobby
- Corridor / return plenum
- Central plant yard

- AHU Air-Handling Unit
- FCU Fan-Coil Unit (FCU)
- Water-cooled chiller
- Cooling tower (induced draft)
- Precision cooling (server room)
- Primary chilled-water pump
- Supply diffuser (4-way)
- Return-air grille
- Zone thermostat (BACnet)

- Return duct (warm air)
- CHW supply 44°F / 7°C
- CHW return 54°F / 12°C
- Condenser water (CW)
- Building / partition wall
- Flow direction arrow
- North arrow


- 1× AHU 15,000 CFM (1 Zone VAV)
- 9× FCUs zone + meeting + amenity
- 2× 150 TR chillers (N+1)
- 1× induced-draft cooling tower
- 3× primary CHW pumps (2W + 1S)
- CHW ΔT 10°F (44°F / 54°F)
- OA: 20 CFM/person ASHRAE 62.1
- Filtration: MERV-13 (AHU) + MERV-8 (FCU)
- Controls: BACnet/Modbus DDC, VAV zone dampers
- Acoustics: NC-35 offices, NC-40 open zones
- Server room: dedicated CRAC N+1, 24/7

- FCU Fan-Coil Unit
- VAV Variable Air Volume
- CRAC Computer Room A/C
- CHW Chilled Water
- CW Condenser Water
- OA Outside Air
- RA Return Air
- SA Supply Air
- TR Ton of Refrigeration
- CFM Cubic Feet / Minute
- DDC Direct Digital Control
- MERV Minimum Efficiency Reporting Value
- NC Noise Criterion
- N+1 One redundant unit

MULTI-ZONE AIR COND

4 office zones + corridor return • 1× AHU (15,000 CFM)

N

 

LEGEND


- Office zone
- Meeting / training
- Server / electrical
- AHU plant room
- Mechanical / pump
- Pantry / breakout
- Reception / lobby
- Corridor / return plenum
- Central plant yard

- AHU Air-Handling Unit
- FCU Fan-Coil Unit (FCU)
- Water-cooled chiller
- Cooling tower (induced draft)
- Precision cooling (server room)
- Primary chilled-water pump
- Supply diffuser (4-way)
- Return-air grille
- Zone thermostat (BACnet)

- Return duct (warm air)
- CHW supply 44°F / 7°C
- CHW return 54°F / 12°C
- Condenser water (CW)
- Building / partition wall
- Flow direction arrow
- North arrow

- 1× AHU 15,000 CFM (1 Zone VAV)
- 9× FCUs zone + meeting + amenity
- 2× 150 TR chillers (N+1)
- 1× induced-draft cooling tower
- 3× primary CHW pumps (2W + 1S)
- CHW ΔT 10°F (44°F / 54°F)
- OA: 20 CFM/person ASHRAE 62.1
- Filtration: MERV-13 (AHU) + MERV-8 (FCU)
- Controls: BACnet/Modbus DDC, VAV zone dampers
- Acoustics: NC-35 offices, NC-40 open zones
- Server room: dedicated CRAC N+1, 24/7


- FCU Fan-Coil Unit
- VAV Variable Air Volume
- CRAC Computer Room A/C
- CHW Chilled Water
- CW Condenser Water
- OA Outside Air
- RA Return Air
- SA Supply Air
- TR Ton of Refrigeration
- CFM Cubic Feet / Minute
- DDC Direct Digital Control
- MERV Minimum Efficiency Reporting Value
- NC Noise Criterion
- N+1 One redundant unit

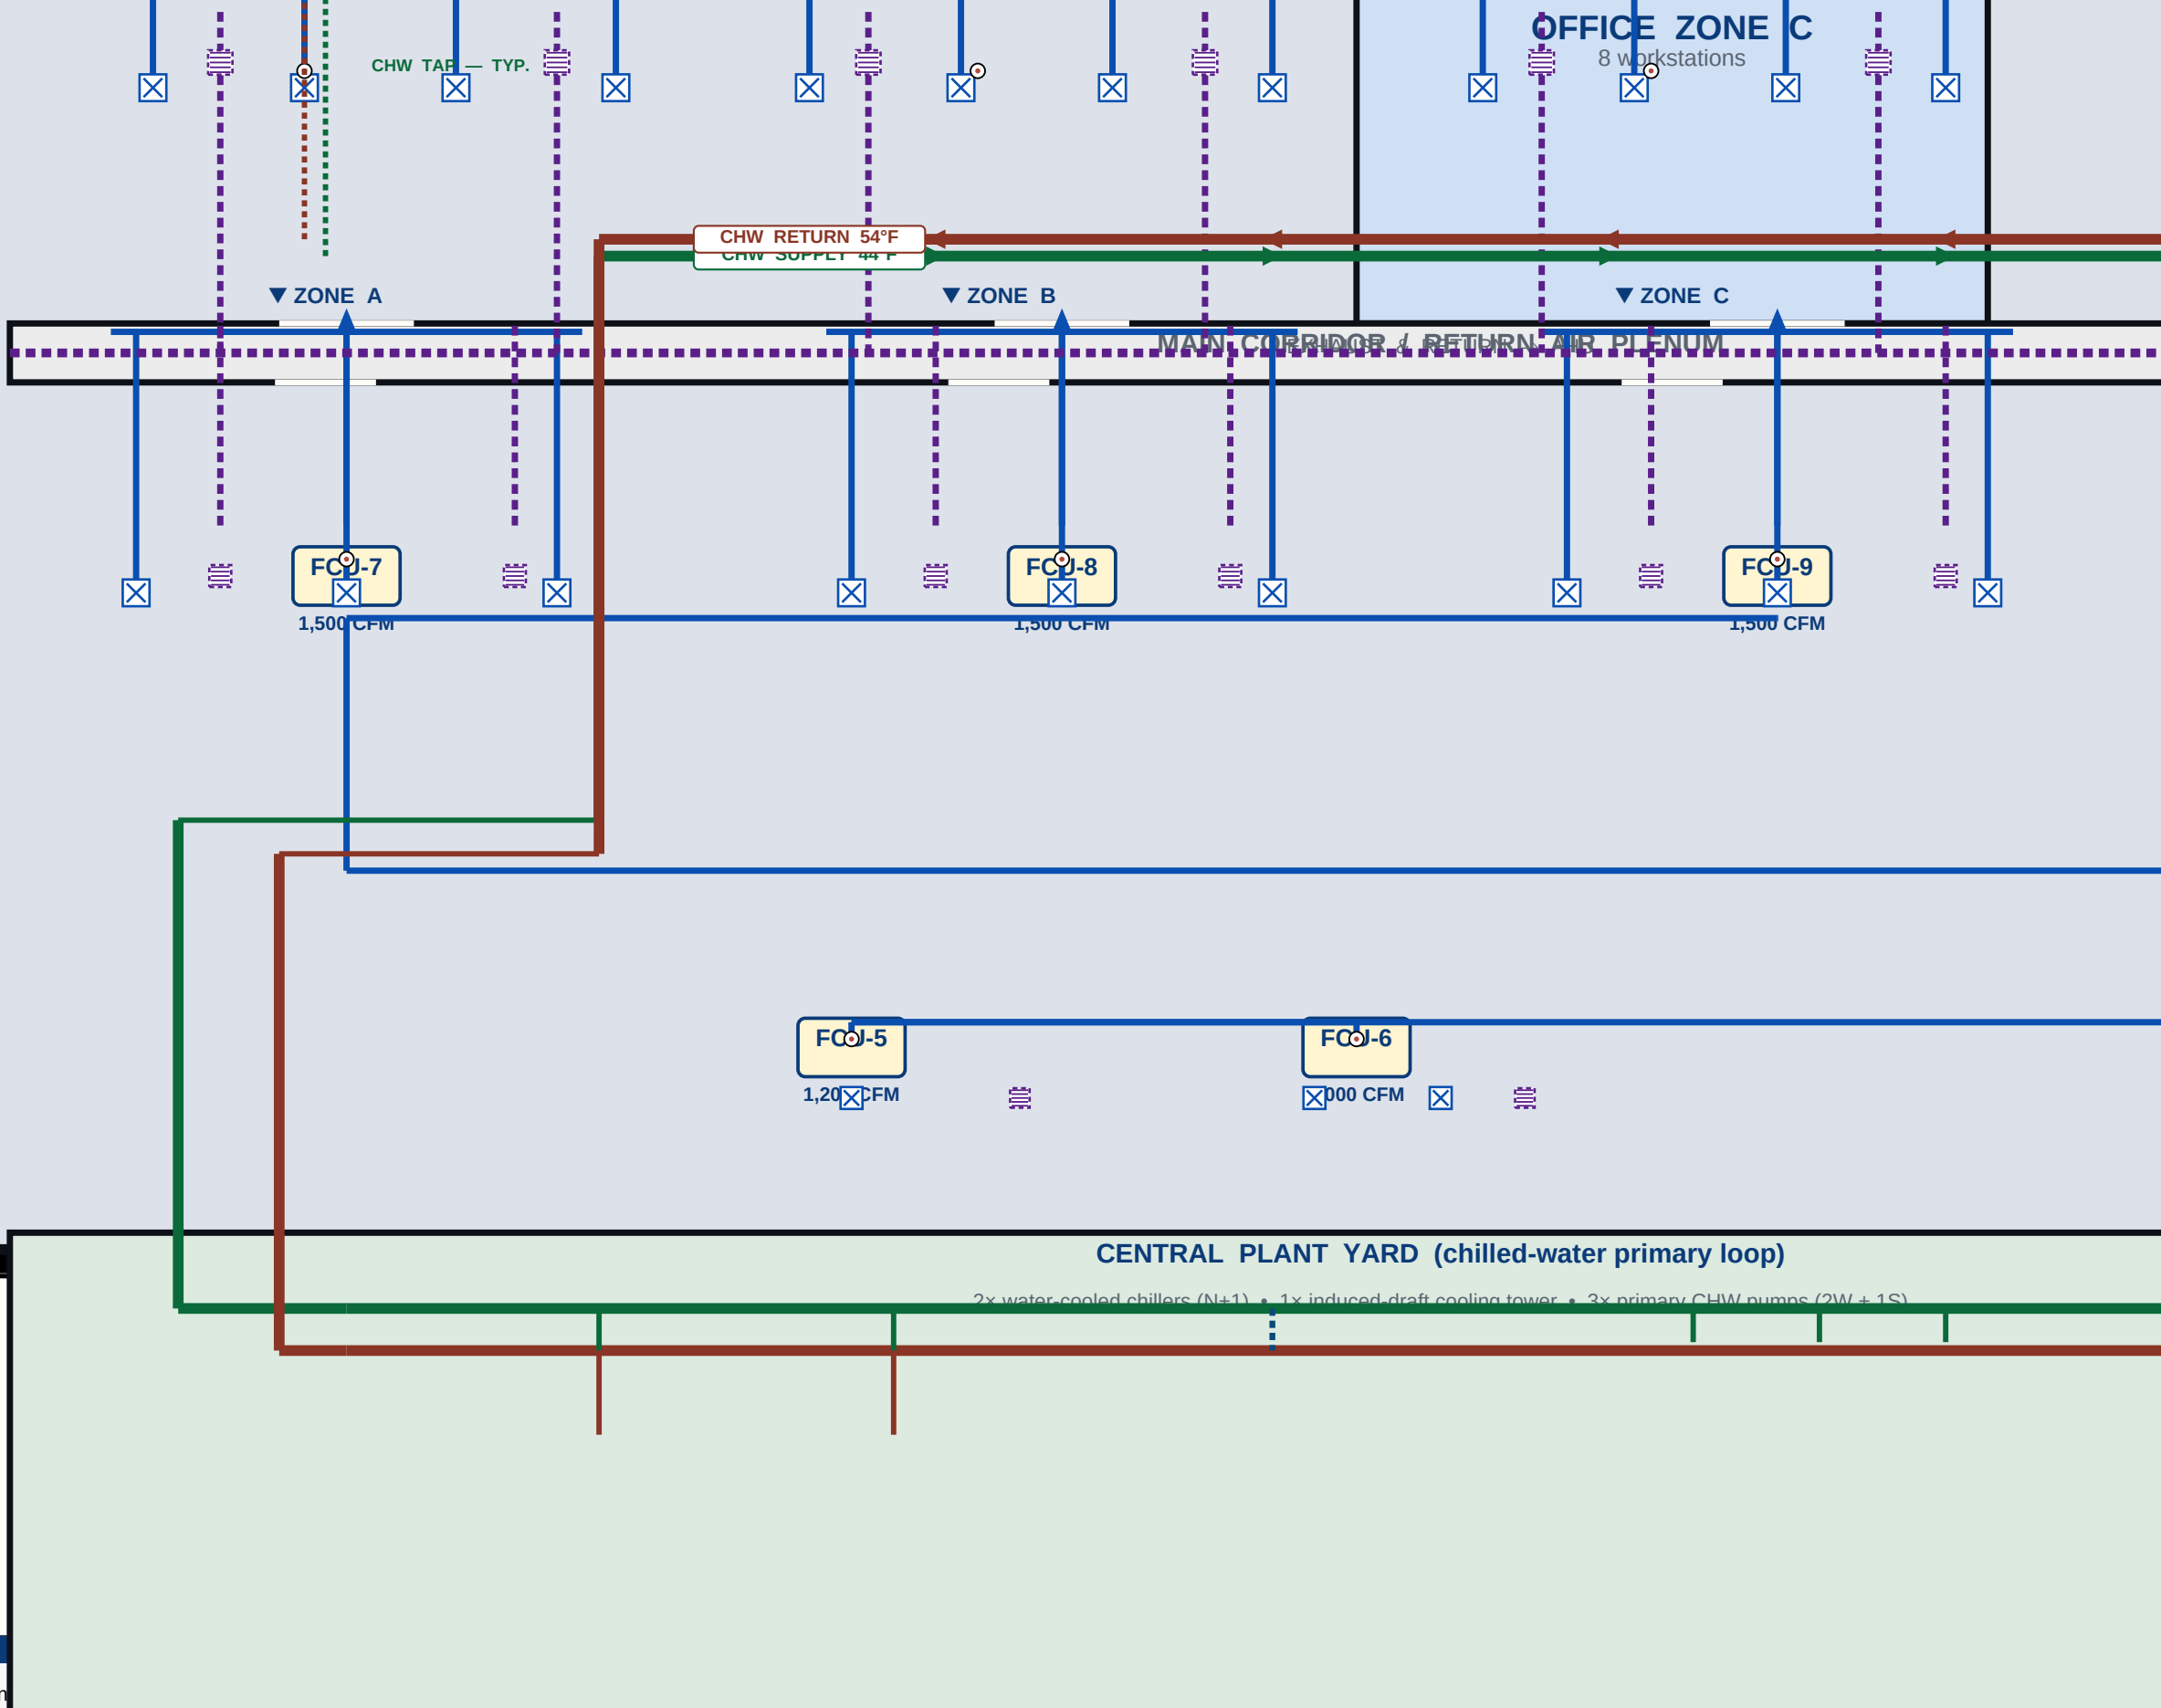

MULTI-ZONE AIR

4 office zones + corridor return • 1× AHU

N

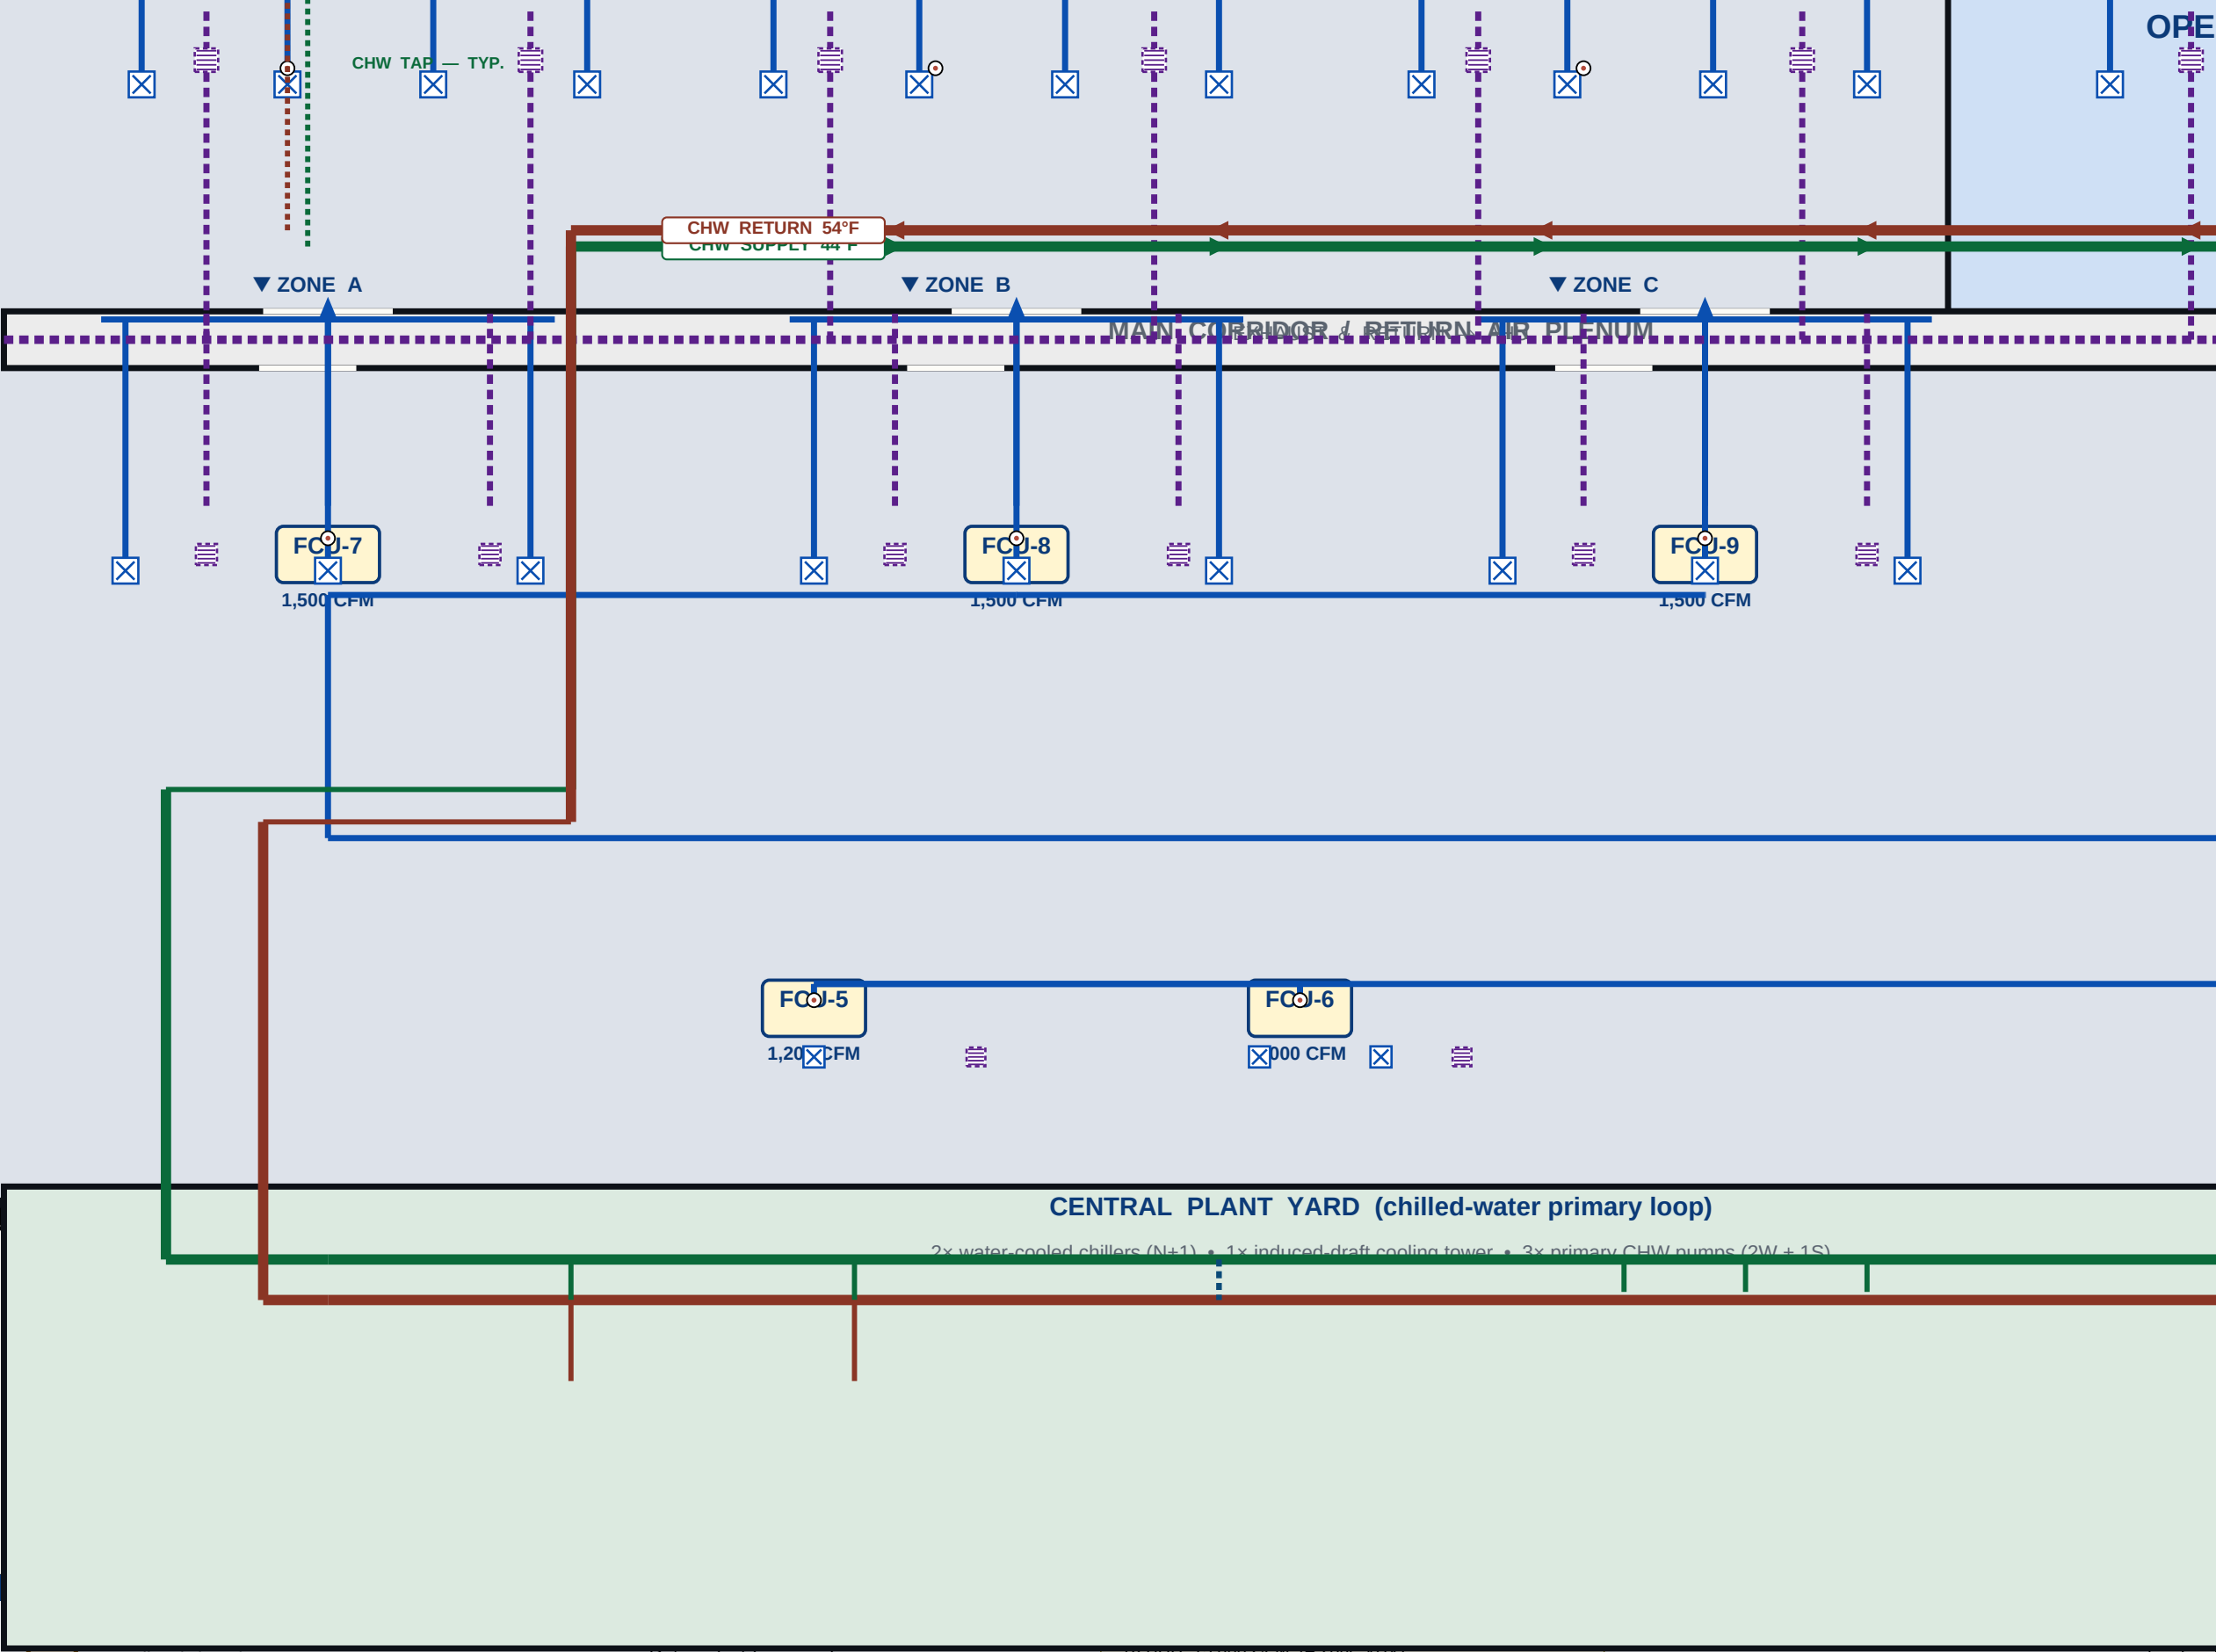

LEGEND


- Office zone
- Meeting / training
- Server / electrical
- AHU plant room
- Mechanical / pump
- Pantry / breakout
- Reception / lobby
- Corridor / return plenum
- Central plant yard

- Fan-Coil Unit (FCU)
- Water-cooled chiller
- Cooling tower (induced draft)
- Precision cooling (server room)
- Primary chilled-water pump
- Supply diffuser (4-way)
- Return-air grille
- Zone thermostat (BACnet)

- Return duct (warm air)
- CHW supply 44°F / 7°C
- CHW return 54°F / 12°C
- Condenser water (CW)
- Building / partition wall
- Flow direction arrow
- North arrow

- 1× AHU 10,000 CFM (1 Zone VAV)
- 9× FCUs zone + meeting + amenity
- 2× 150 TR chillers (N+1)
- 1× induced-draft cooling tower
- 3× primary CHW pumps (2W + 1S)
- CHW ΔT 10°F (44°F / 54°F)
- OA: 20 CFM/person ASHRAE 62.1
- Filtration: MERV-13 (AHU) + MERV-8 (FCU)
- Controls: BACnet/Modbus DDC, VAV zone dampers
- Acoustics: NC-35 offices, NC-40 open zones
- Server room: dedicated CRAC N+1, 24/7

- FCU Fan-Coil Unit
- VAV Variable Air Volume
- CRAC Computer Room A/C
- CHW Chilled Water
- CW Condenser Water
- OA Outside Air
- RA Return Air
- SA Supply Air
- TR Ton of Refrigeration
- CFM Cubic Feet / Minute
- DDC Direct Digital Control
- MERV Minimum Efficiency Reporting Value
- NC Noise Criterion
- N+1 One redundant unit

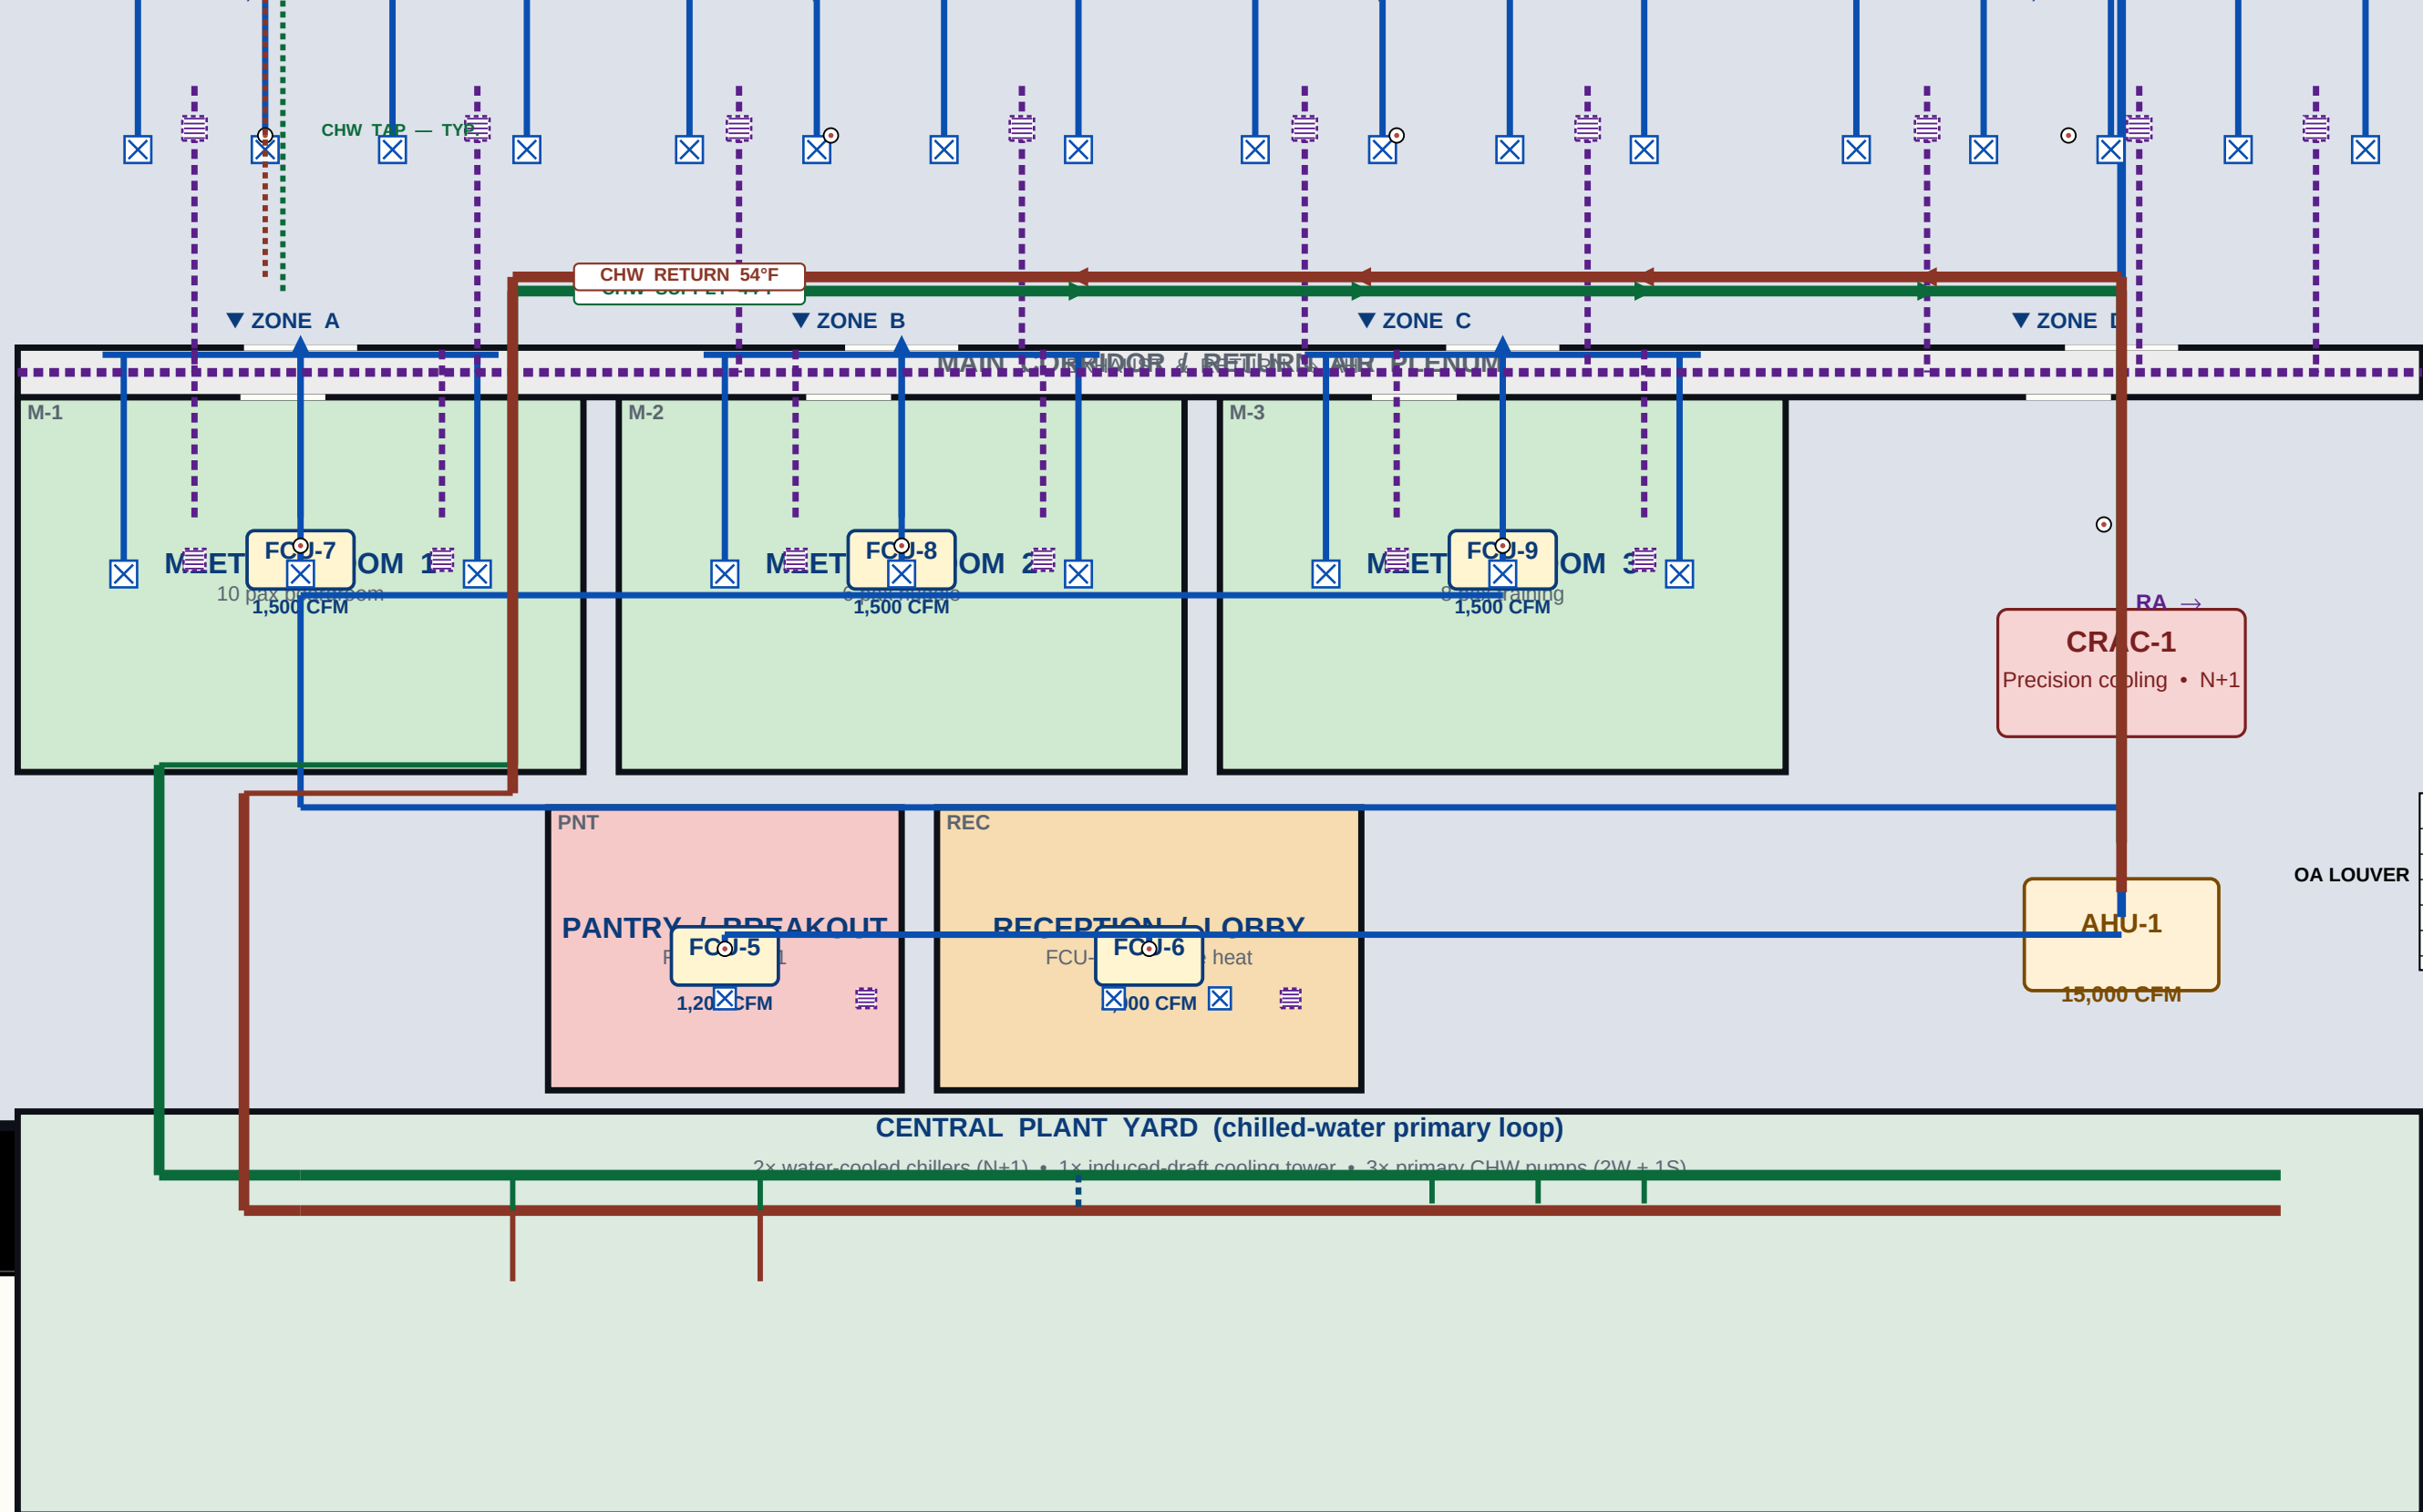

LEGEND

- Office zone
- Meeting / training
- Server / electrical
- AHU plant room
- Mechanical / pump
- Pantry / breakout
- Reception / lobby
- Corridor / return plenum
- Central plant yard

- AHU Air-Handling Unit (AHU)
- FCU Fan-Coil Unit (FCU)
- Water-cooled chiller
- INDUCED DRAFT COOLING TOWER
- Cooling tower (induced draft)
- Precision cooling (server room)
- Primary chilled-water pump
- Supply diffuser (4-way)
- Return-air grille
- Zone thermostat (BACnet)

- Supply duct (cool air)
- Return duct (warm air)
- CHW supply 44°F / 7°C
- CHW return 54°F / 12°C
- Condenser water (CW)
- Building / partition wall
- Flow direction arrow
- North arrow

- Total cooling load (est.): 28 TR
- 1x AHU 15,000 CFM (4-zone VAV)
- 9x FCUs zone + meeting + amenity
- 2x 150 TR chillers (N+1)
- 1x induced-draft cooling tower
- 3x primary CHW pumps (2W + 1S)
- CHW ΔT 10°F (44°F / 54°F)
- OA: 20 CFM/person ASHRAE 62.1
- Filtration: MERV-13 (AHU) + MERV-8 (FCU)
- Controls: BACnet/Modbus DDC, VAV zone dampers
- Acoustics: NC-35 offices, NC-40 open zones
- Server room: dedicated CRAC N+1, 24/7


DEMO / PITCH REFERENCE — NOT FOR CONSTRUCTION

- AHU Air-Handling Unit
- FCU Fan-Coil Unit
- VAV Variable Air Volume
- CRAC Computer Room A/C
- CHW Chilled Water
- CW Condenser Water
- OA Outside Air
- RA Return Air
- SA Supply Air
- TR Ton of Refrigeration
- CFM Cubic Feet / Minute
- DDC Direct Digital Control
- MERV Minimum Efficiency Reporting Value
- NC Noise Criterion
- N+1 One redundant unit

+ AMENITY
g units: millimetres

MULTI-ZONE AIR CONDITIONING — SAMPLE FLOOR PLAN

4 office zones + corridor return • 1× AHU (15,000 CFM) + 9× FCUs • Chilled-water primary plant (2× 150 TR + induced-draft tower)

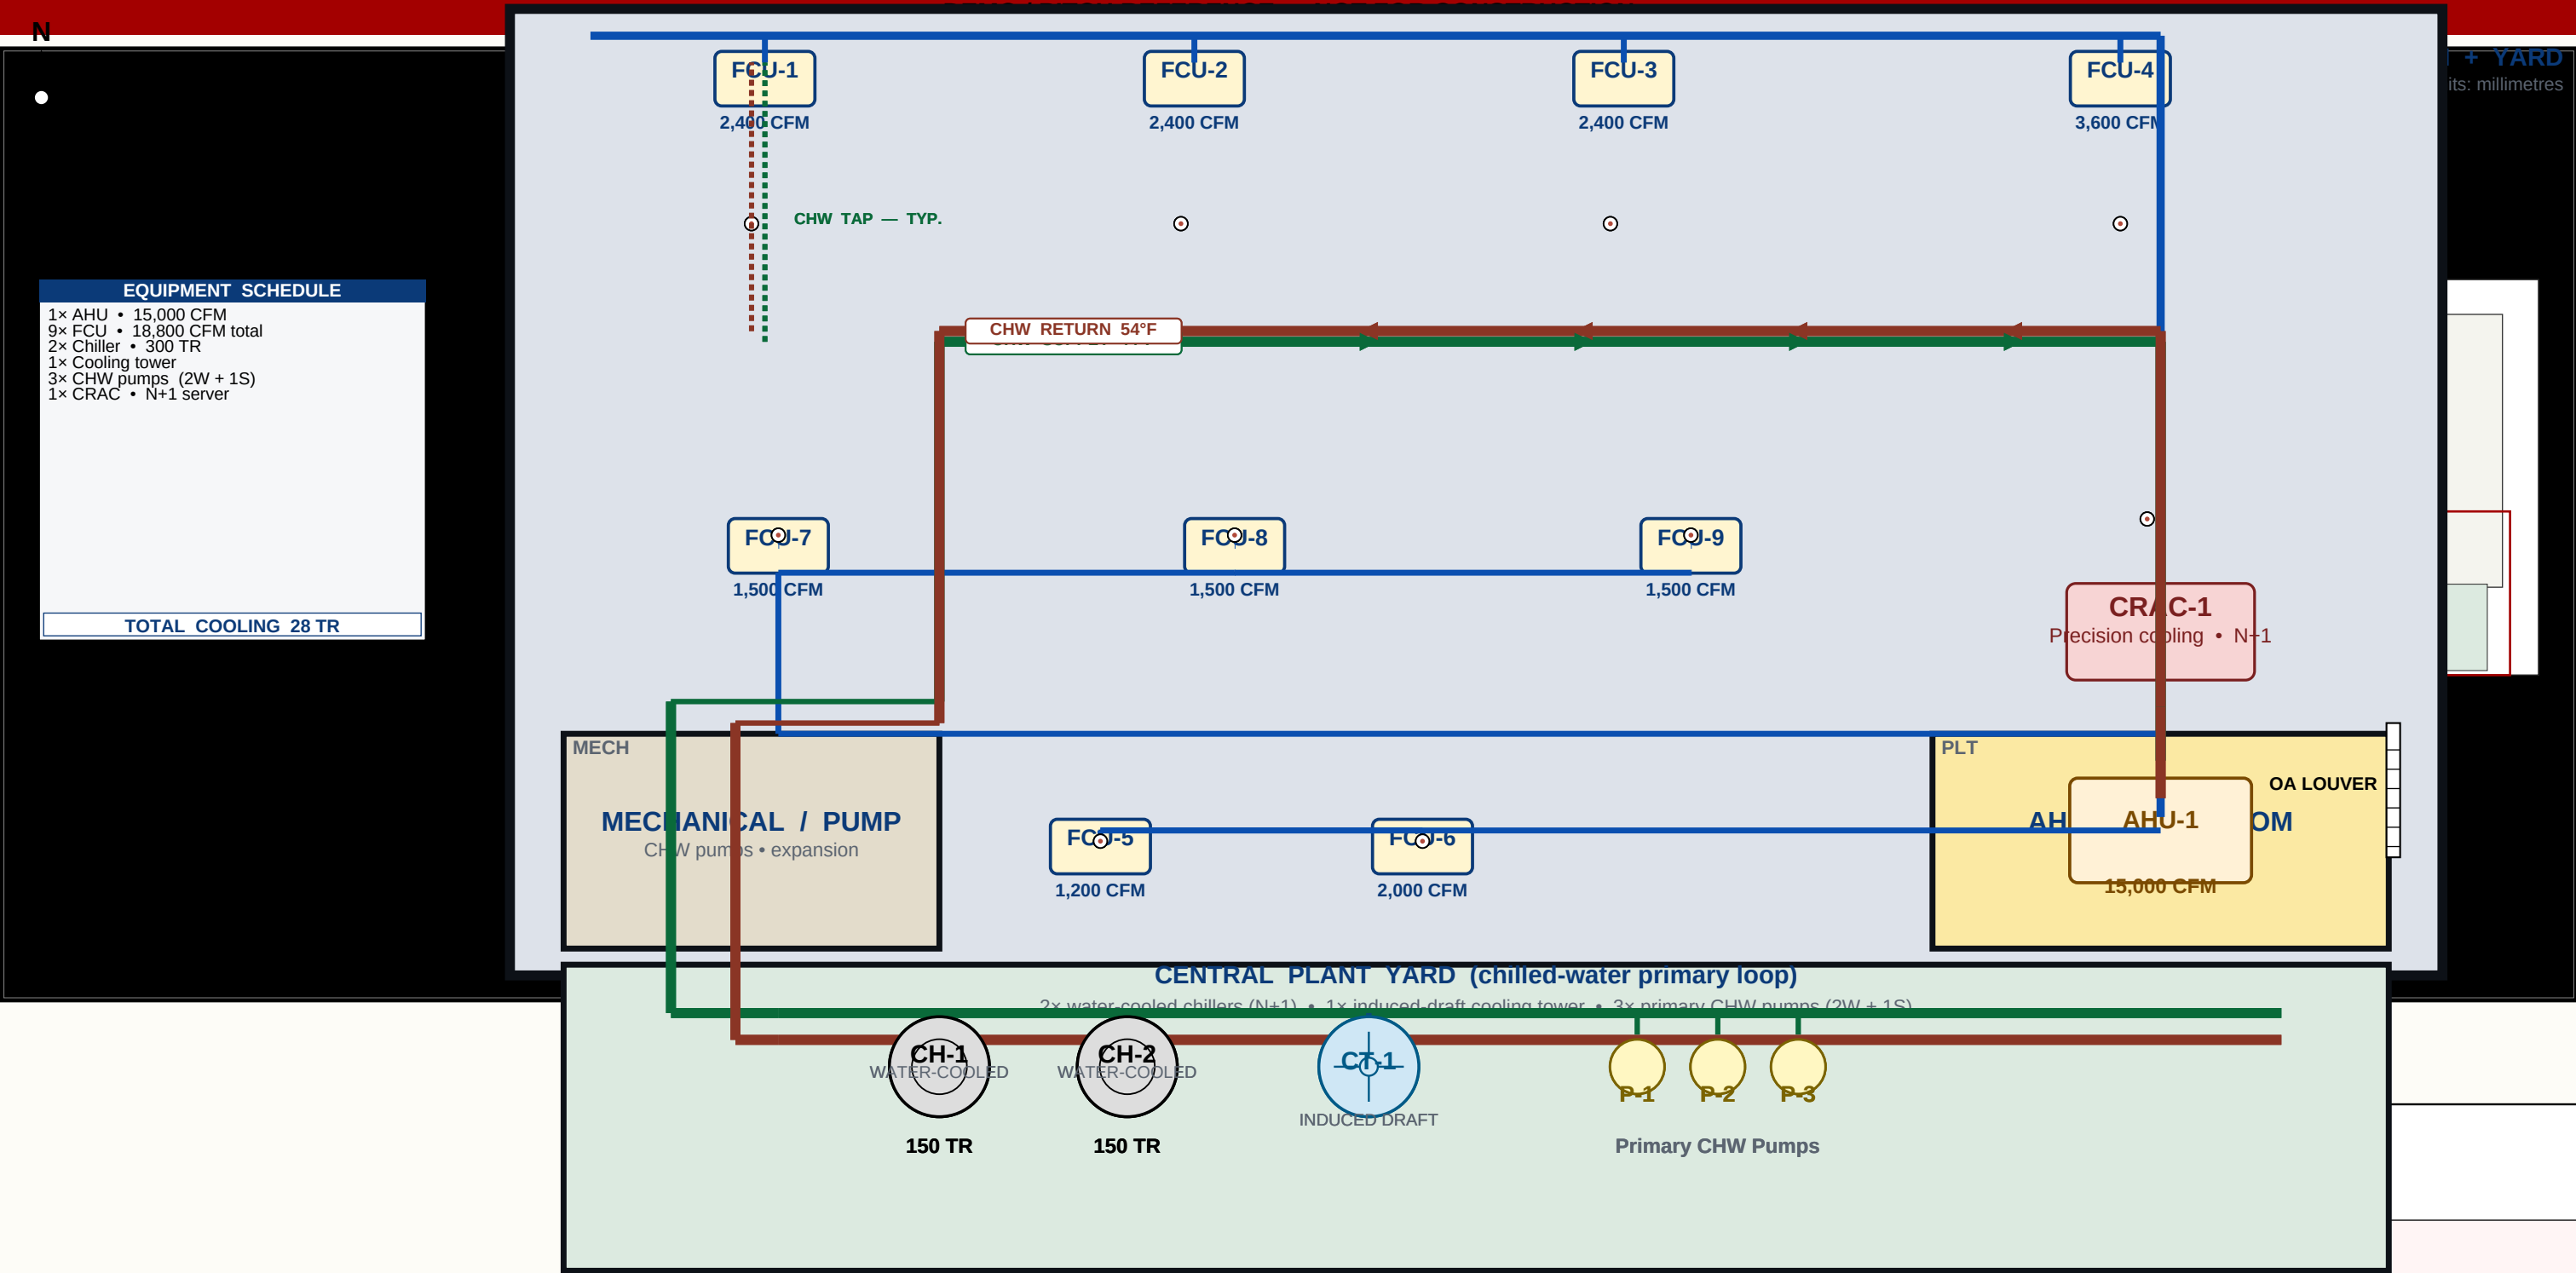

LEGEND

- Office zone
- Meeting / training
- Server / electrical
- AHU plant room
- Mechanical / pump
- Pantry / breakout
- Reception / lobby
- Corridor / return plenum
- Central plant yard

- AHU Air-Handling Unit (AHU)
- FCU Fan-Coil Unit (FCU)
- Water-cooled chiller
- Cooling tower (induced draft)
- Precision cooling (server room)
- Primary chilled-water pump
- Supply diffuser (4-way)
- Return-air grille
- Zone thermostat (BACnet)

- Supply duct (cool air)
- Return duct (warm air)
- CHW supply 44°F / 7°C
- CHW return 54°F / 12°C
- Condenser water (CW)
- Building / partition wall
- Flow direction arrow
- North arrow

- Total cooling load (est.): 28 TR
- 1× AHU 15,000 CFM (4-zone VAV)
- 9× FCUs zone + meeting + amenity
- 2× 150 TR chillers (N+1)
- 1× induced-draft cooling tower
- 3× primary CHW pumps (2W + 1S)
- CHW ΔT 10°F (44°F / 54°F)
- OA: 20 CFM/person ASHRAE 62.1
- Filtration: MERV-13 (AHU) + MERV-8 (FCU)
- Controls: BACnet/Modbus DDC, VAV zone dampers
- Acoustics: NC-35 offices, NC-40 open zones
- Server room: dedicated CRAC N+1, 24/7

DEMO / PITCH REFERENCE — NOT FOR CONSTRUCTION

- AHU Air-Handling Unit
- FCU Fan-Coil Unit
- VAV Variable Air Volume
- CRAC Computer Room A/C
- CHW Chilled Water
- CW Condenser Water
- OA Outside Air
- RA Return Air
- SA Supply Air
- TR Ton of Refrigeration
- CFM Cubic Feet / Minute
- DDC Direct Digital Control
- MERV Minimum Efficiency Reporting Value
- NC Noise Criterion
- N+1 One redundant unit

MULTI-ZONE A

4 office zones + corridor return

N

▼ ZONE A

▼ ZONE B

▼ ZONE C

MAIN CORRIDOR & RETURN AIR PLENUM

FCU-7

1,500 CFM

FCU-8

1,500 CFM

FCU-9

1,500 CFM

FCU-5

1,200 CFM

FCU-6

2,000 CFM

CENTRAL PLANT YARD (chilled-water primary loop)

2x water-cooled chillers (N+1) • 1x induced-draft cooling tower • 3x primary CHW pumps (2W + 1S)

LEGEND

- Office zone
- Meeting / training
- Server / electrical
- AHU plant room
- Mechanical / pump
- Pantry / breakout
- Reception / lobby
- Corridor / return plenum
- Central plant yard

- Supply diffuser (4-way)
- Return-air grille
- Zone thermostat (BACnet)

- Flow direction arrow
- North arrow

- Controls: BACnet/Modbus DDC, VAV zone dampers
- Acoustics: NC-35 offices, NC-40 open zones
- Server room: dedicated CRAC N+1, 24/7

- SA Supply Air
- TR Ton of Refrigeration
- CFM Cubic Feet / Minute
- DDC Direct Digital Control
- MERV Minimum Efficiency Reporting Value
- NC Noise Criterion
- N+1 One redundant unit